


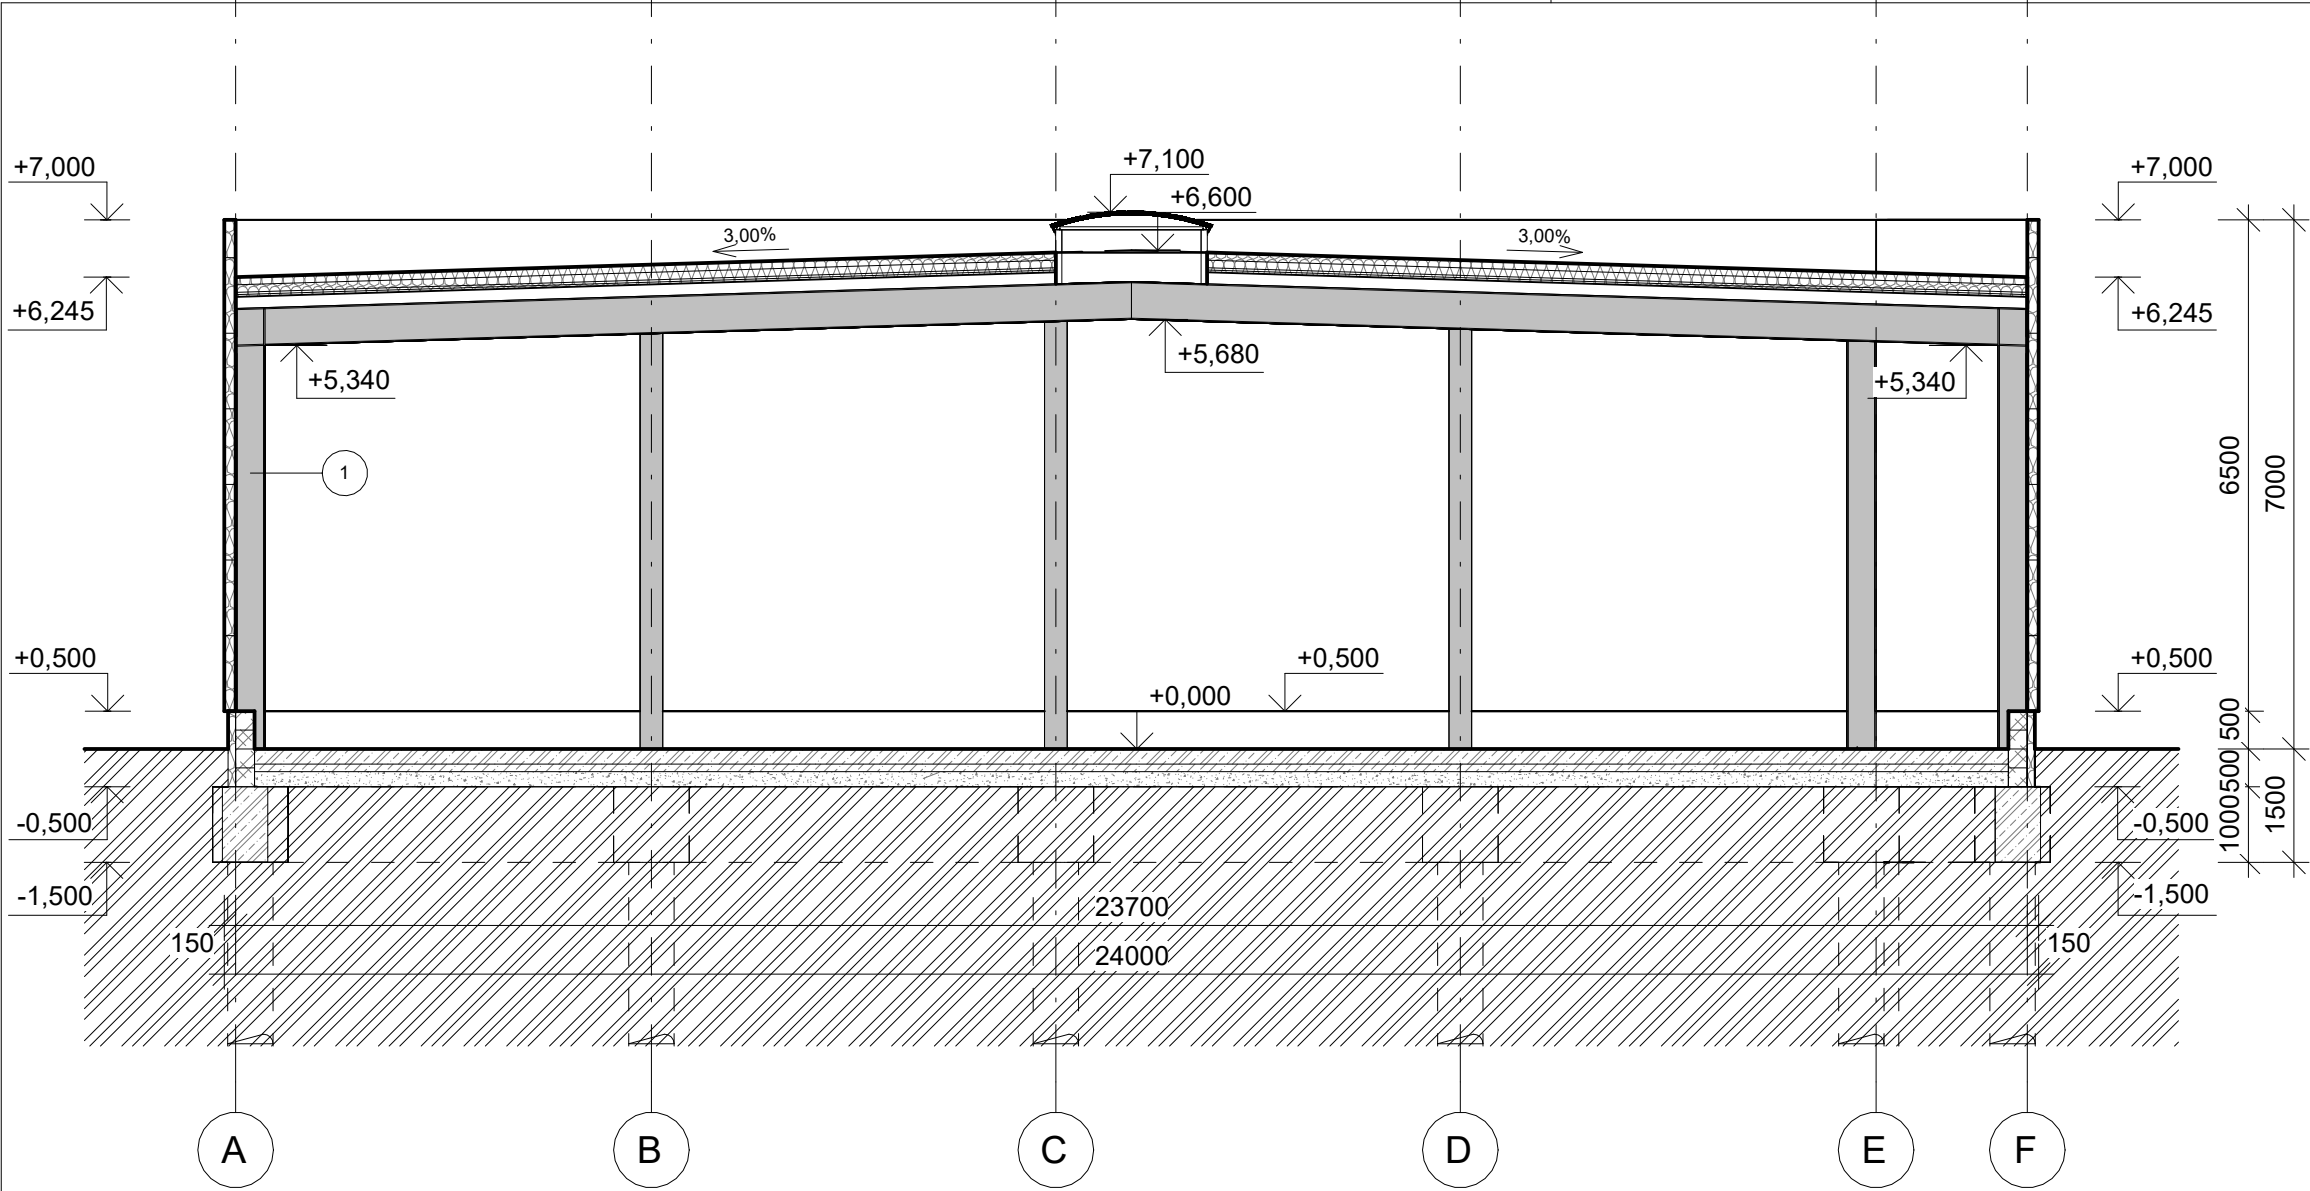

LEGENDA MATERIÁLU:

- TEPELNÁ IZOLACE
- BETON
- TVÁRNICE ZTRACENÉHO BEDNĚNÍ TL. 250 mm, VÝŠKY 250 mm
- PŮVODNÍ TERÉN

LEGENDA ODKAZŮ:

1 - OCELOVÁ KONSTRUKCE

±0,000 = XXX,XX m.n.m. (Bpv)



RIVESTA Consult s.r.o.

Panská 25, 686 04 Kunovice
IČO: 07461674
www.rivesta.cz

Akce: YEZEDO KOSTICE

Investor: Obec Kostice,
nám. Osvobození 445/14,
691 52 Kostice

Místo stavby: k.ú.Kostice [670588]

Vypracoval: Bc. RADEK JURČEK
TOMÁŠ HOUDEK

Stupeň PD: STUDIE

Číslo zakázky: 2026_012

Datum: 07/2026

Stavební objekt SO: SO03 (D.III) VÝROBNÍ HALA

Měřítko: 1:100

Část dokumentu: DNS 01.02 ŘEZ 1-1'